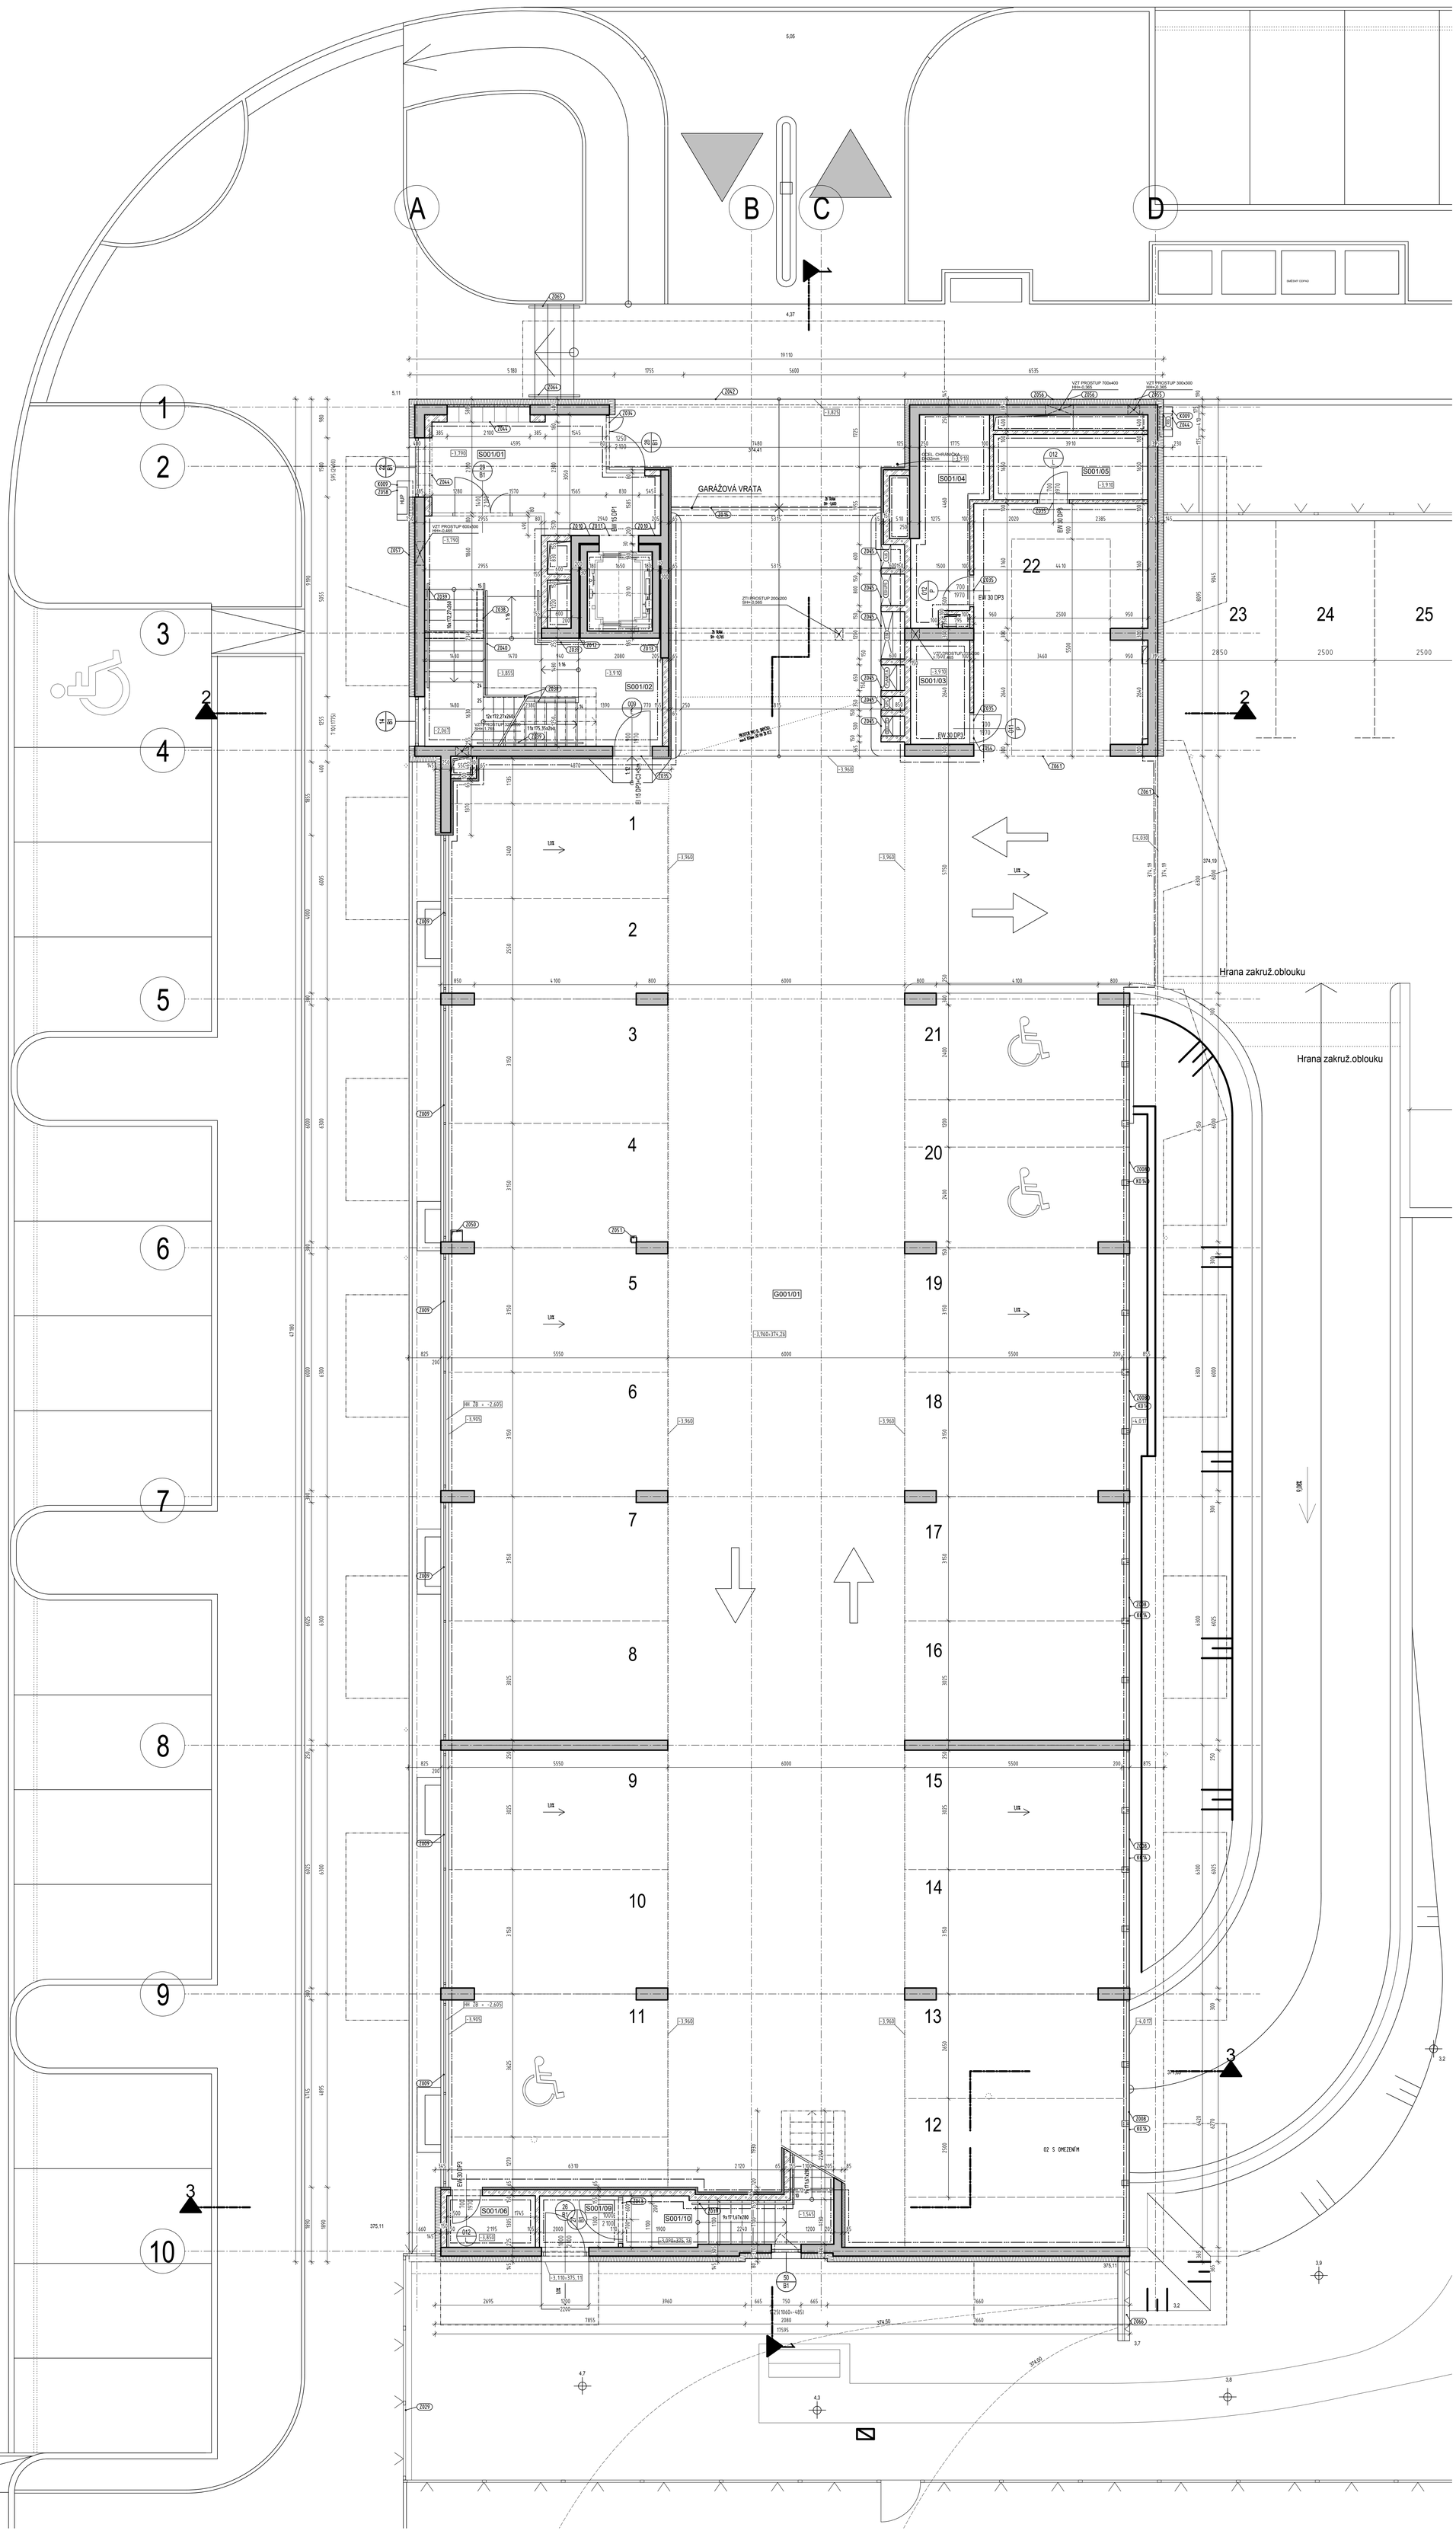

LEGENDA MÍSTNOSTÍ

Č. M.	ÚČEL MÍSTNOSTI	m2		PODLAHA
GARÁŽ				
G001/01	PARKING	694.71	P34	nulová systémová podlaha viz. TZ
CELKEM		694.71		
SKLEPY				
S001/04	SKLEP	8.20	P36	betonová mazanina + uzavírací nátěr
S001/05	SKLEP	6.52	P36	betonová mazanina + uzavírací nátěr
S001/06	SKLEP	2.86	P36	betonová mazanina + uzavírací nátěr
CELKEM		17.58		
SPOLEČNÉ PROSTORY				
S001/01	VSTUPNÍ HALA	13.79	P30	keramická dlažba včetně soklu
S001/02	CHODBA+SCHODIŠTĚ	25.78	P30, P60, P63	keramická dlažba včetně soklu
S001/03	UPS	4.03	P36	betonová mazanina + uzavírací nátěr
S001/09	ZÁDVEŘÍ	2.75	P30	keramická dlažba včetně soklu
S001/10	CHODBA+SCHODIŠTĚ	8.70	P30, P60, P63	keramická dlažba včetně soklu
CELKEM		55.05		

LEGENDA MATERIÁLŮ

- ŽELEZOBETONOVÉ KONSTRUKCE - VIZ STATICKÁ ČÁST
- ZDIVO PŘÍČEK Z KERAMICKÝCH TVAROVEK POROTHERM 8 P+D, P8, NA M/VC, M5 PRO TL. PŘÍČKY 115MM ZDIVO PŘÍČEK Z KERAMICKÝCH TVAROVEK POROTHERM 11,5 P+D, P8, NA M/VC, M5 PRO TL. PŘÍČKY 145MM
- ZDIVO Z CHEL PLNÝCH PÁLENÝCH CP P10, 290/140/65 NA MALTU MC, M5. PRO TL. PŘÍČKY 155MM, 170MM
- PŘIZDÍVKA Z TVÁRNIC YTONG (tl. 100, 150, 180mm) LEPENÝCH TMELEM
- ZDIVO ZE ZDÍCÍCH BLOKŮ LIAPOR M240/12/1200, M5, NA MC, TL. ZDIVA 240MM A 270MM., MEZIBYTOVÁ STĚNA ZDIVO ZE ZDÍCÍCH BLOKŮ LIAPOR M175/6/1300, M5, NA MC, TL. ZDIVA 190MM OBEZDÍVKA INSTALAČNÍCH JADER
- OBVODOVÝ PLÁŠŤ Z KERAMICKÝCH TVAROVEK POROTHERM 24 P+D, TŘ.900, P15, NA MALTU M/VC, M10 + KONTAKTNÍ ZATEPLOVACÍ SYSTÉM
- SDK PŘÍČKA S MINERÁLNÍ IZOLACÍ
- ZDIVO PŘÍČEK Z KERAMICKÝCH TVAROVEK POROTHERM 11,5 AKU, P10, NA MALTU M/VC, M5 PRO TL. PŘÍČKY 145MM
- POŽÁRNÍ ÚSEKY

OBJEKT B1 ± 0,000 = 378,22 m.n.m

ZÁPADNÍ MĚSTO
ZÁPADNÍ ČÁST
OBJEKT B1
DOKUMENTACE PRO PROVEDENÍ STAVBY

výškový systém b.p.v., souřadnicový systém S - JTSK

INVESTOR

N.J.B. real a.s.
Václavské náměstí 1
Praha 1
110 00

Razítko :
Schválil:

GENERÁLNÍ PROJEKTANT, ARCHITEKT

ADR
Libeňská 3127/1
Praha 5
150 00
tel.: 257 210 252
fax.: 257 210 244
E-mail: adr@adr.cz

Schválil :
Mgr. A. Aleš Lapka

Vypracoval :
Ing. Arch. Ivo Bartoněk
Ing. Arch. Jana Kynčlová

HLAVNÍ INŽENÝR PROJEKTU

building s.r.o.
Packova 13
Praha 8
186 00
tel.: 224 816 566
fax.: 224 813 219
E-mail: building@building-srozz

Schválil :
Ing. Zdeněk Mužka

Hlavní inženýr projektu :
Ing. Miroslav Pařízka

PROJEKTANT ČÁSTI DOKUMENTACE

building s.r.o.
Packova 13
Praha 8
186 00
tel.: 224 816 566
fax.: 224 813 219
E-mail: building@building-srozz

Razítko :

Vypracoval :
Ing. Miroslav Pařízka
Ing. Petr Šmergl

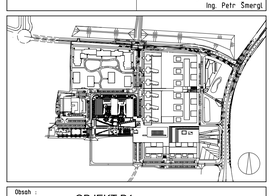

Obsah :
OBJEKT B1
PŮDORYS 1.PP

První datum :	Aktuál. datum :	MĚŘÍTKO :	Počet A4 :	Č. paré :
15/08/2012	10/01/2013	1:50	25xA4	

Projekt	Část projektu	Profese	Druh výkresu	Oblast stavby								Pořadí	Pár. č.Číslování
ZMZ	DPS	ARC	PUD	B1	-	-	-	-	-	0	0	1	0 3 A

PROGRESIV SF BUILDING s.r.o. KLÁŠTERNÍ 20, PRAHA 3, 130 00
Tel.: +420 221 719 021, fax.: +420 224 813 279, www.building-srozz